
SDI PLANTA NIVEL DE CANCHA
SISTEMA DE DETECCIÓN DE INCENDIOS

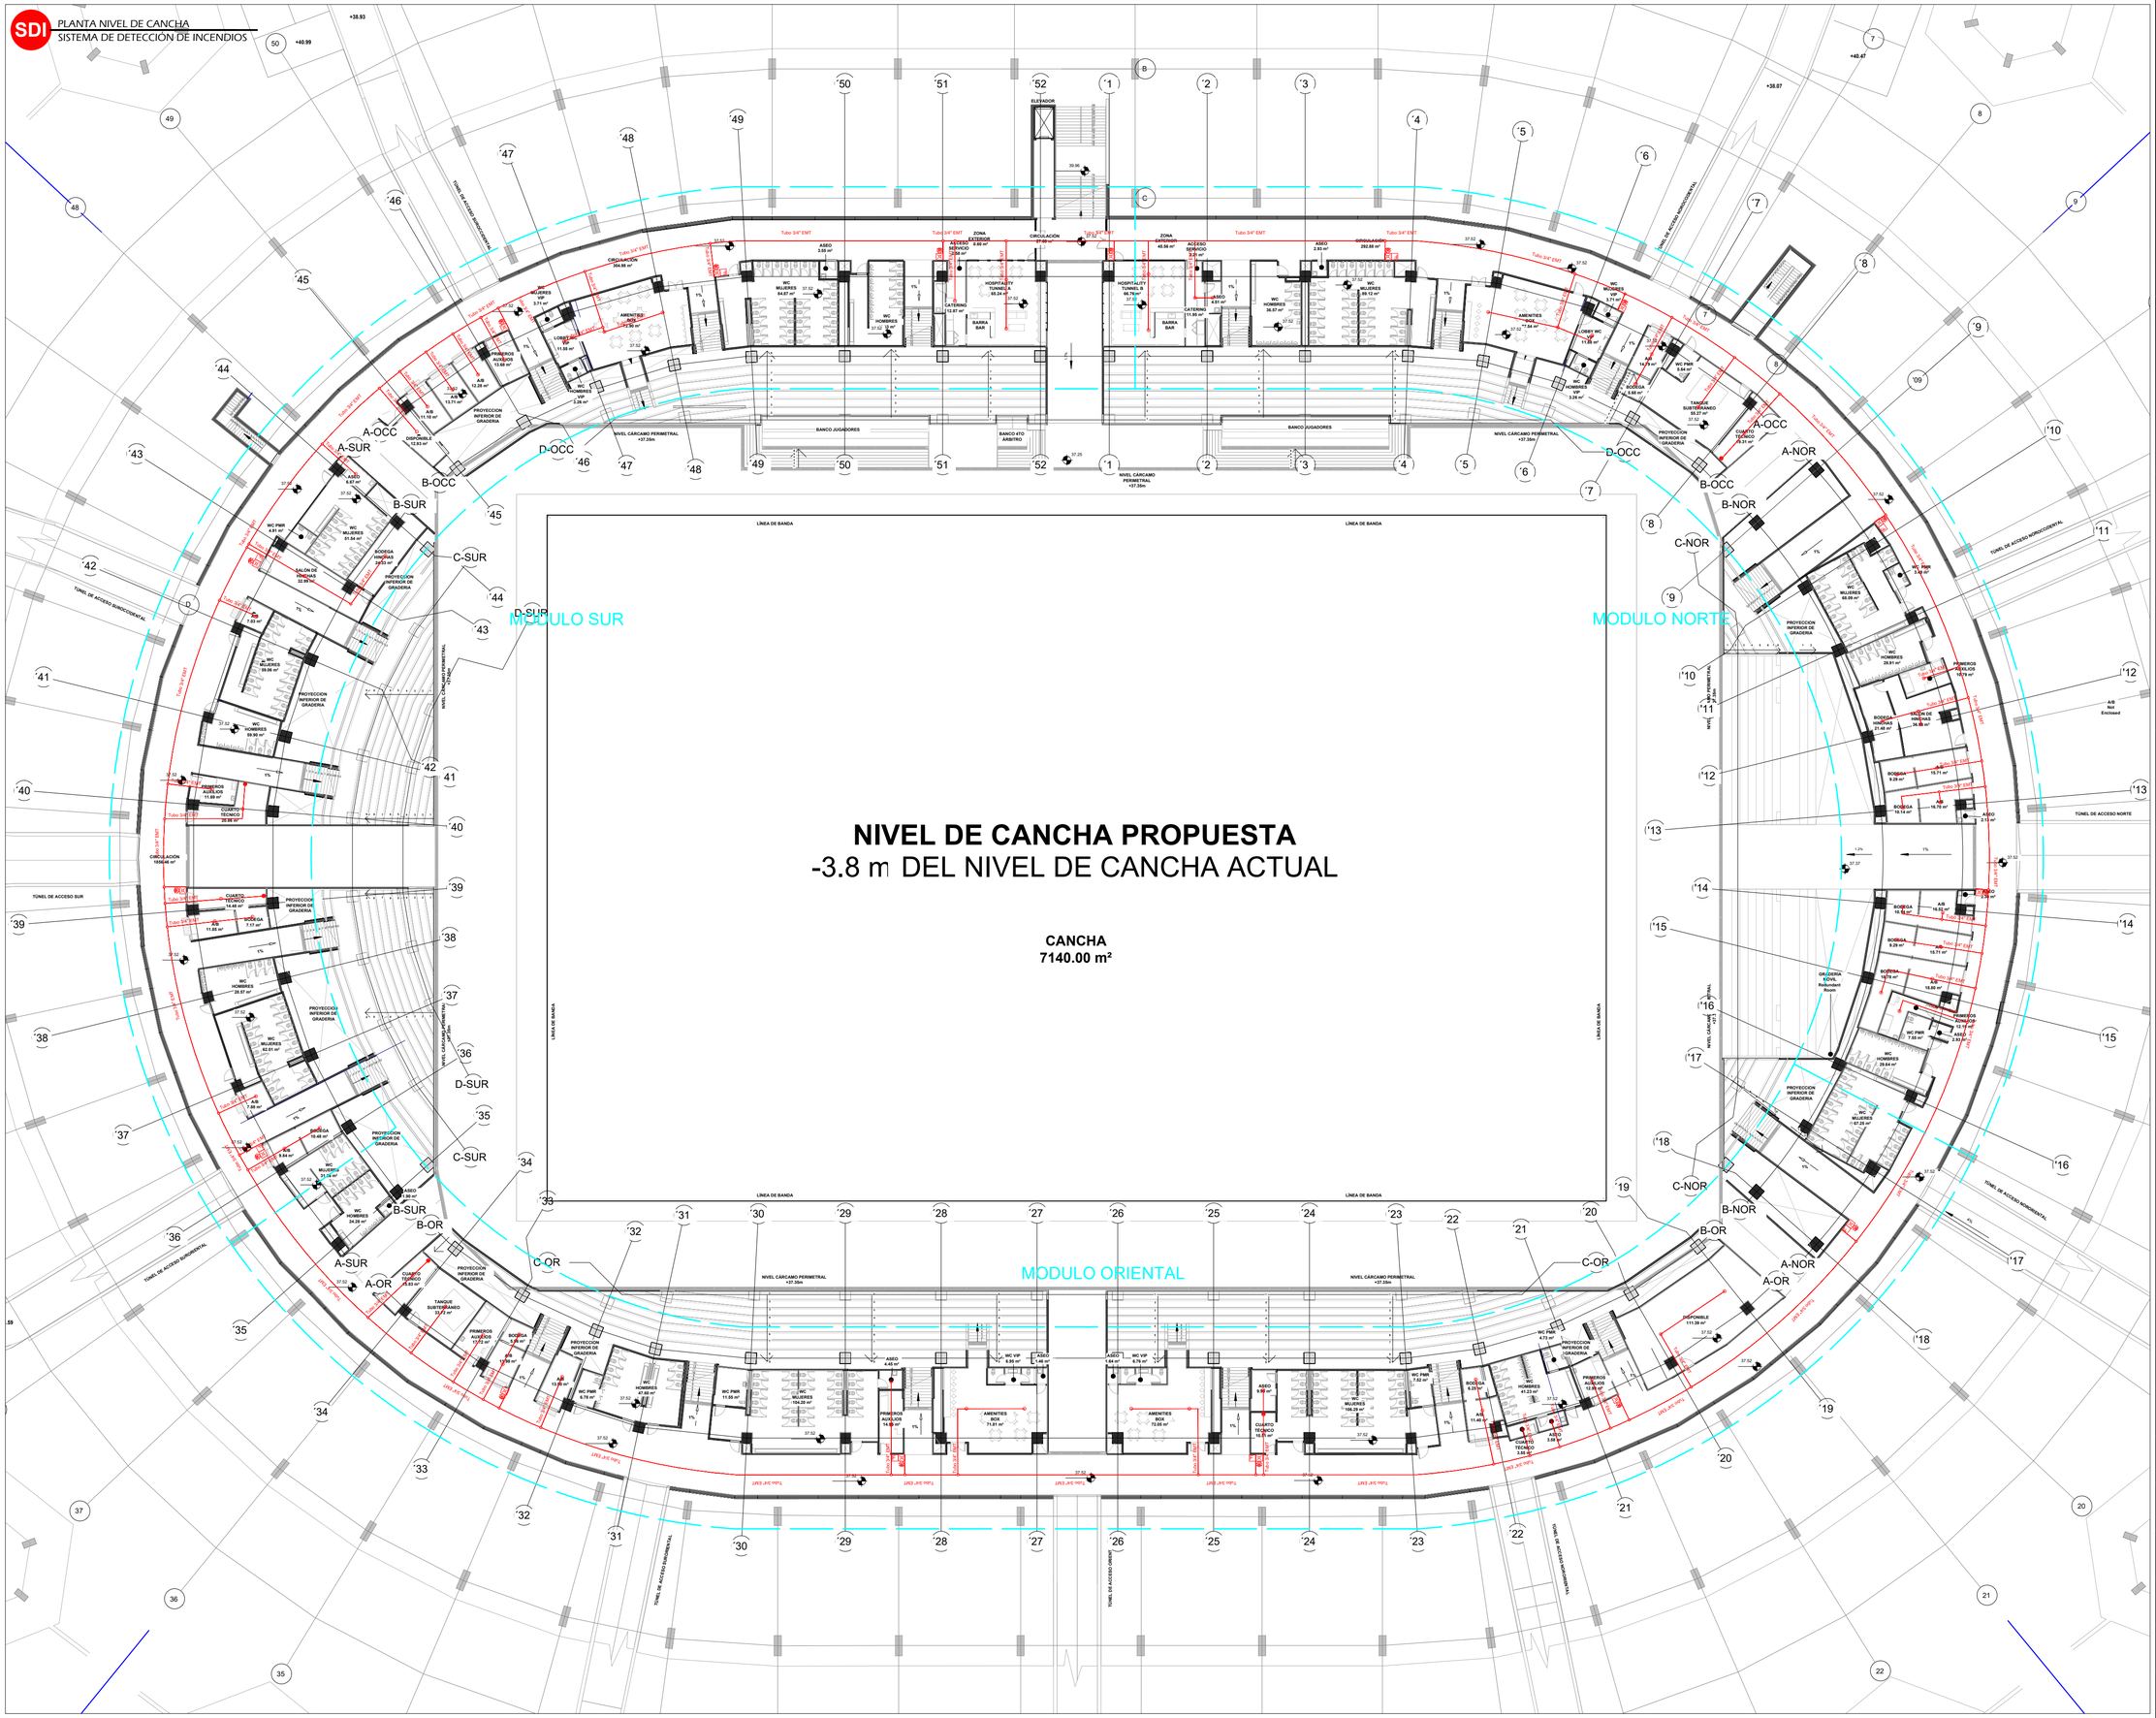

NIVEL DE CANCHA PROPUESTA
-3.8 m DEL NIVEL DE CANCHA ACTUAL

CANCHA
7140.00 m²

GRUPO INTEGRA
Confianza que conecta.
Ingeniería que protege.

PROYECTO:
SISTEMA DE DETECCIÓN DE INCENDIOS

UBICACIÓN:
Calle 46 #1 Sur-45, Barranquilla, Atlántico

CONTIENE:
NIVEL 1 - NIVEL DE CANCHA

SISTEMA:
SISTEMA DE DETECCIÓN DE INCENDIOS

CONVENCIONES:

——	Tuberia EMT ¾"
HCO	Detector Térmico y CO
SH	Detector Humo y Térmico
S	Detector Humo
H	Detector Térmico
F	Estación Manual
G	Detector de GAS
AM	Modulo Monitor
ACM	Modulo de control o Relé
	Parlante-Estrobo
	Parlante de techo
	Caja de 4"x4"
	Registro 50cm x 50cm
FACP	Panel de Incendio
AR	Anunciador remoto

DISEÑO:
Ing. Carlos Correa

DIBUJÓ:
Arq. Yahir Ortega Alvarez

REVISIÓN:
Ing. Nicolás Mussa

FECHA:
ABRIL - 2026

ESCALA:
1:350

PLANCHA No.:
3 - 6

ARCHIVO:
SDI_ROBERTO MELENDEZ 2026