
SDI PLANTA NIVEL DE CANCHA
SISTEMA DE DETECCIÓN DE INCENDIOS

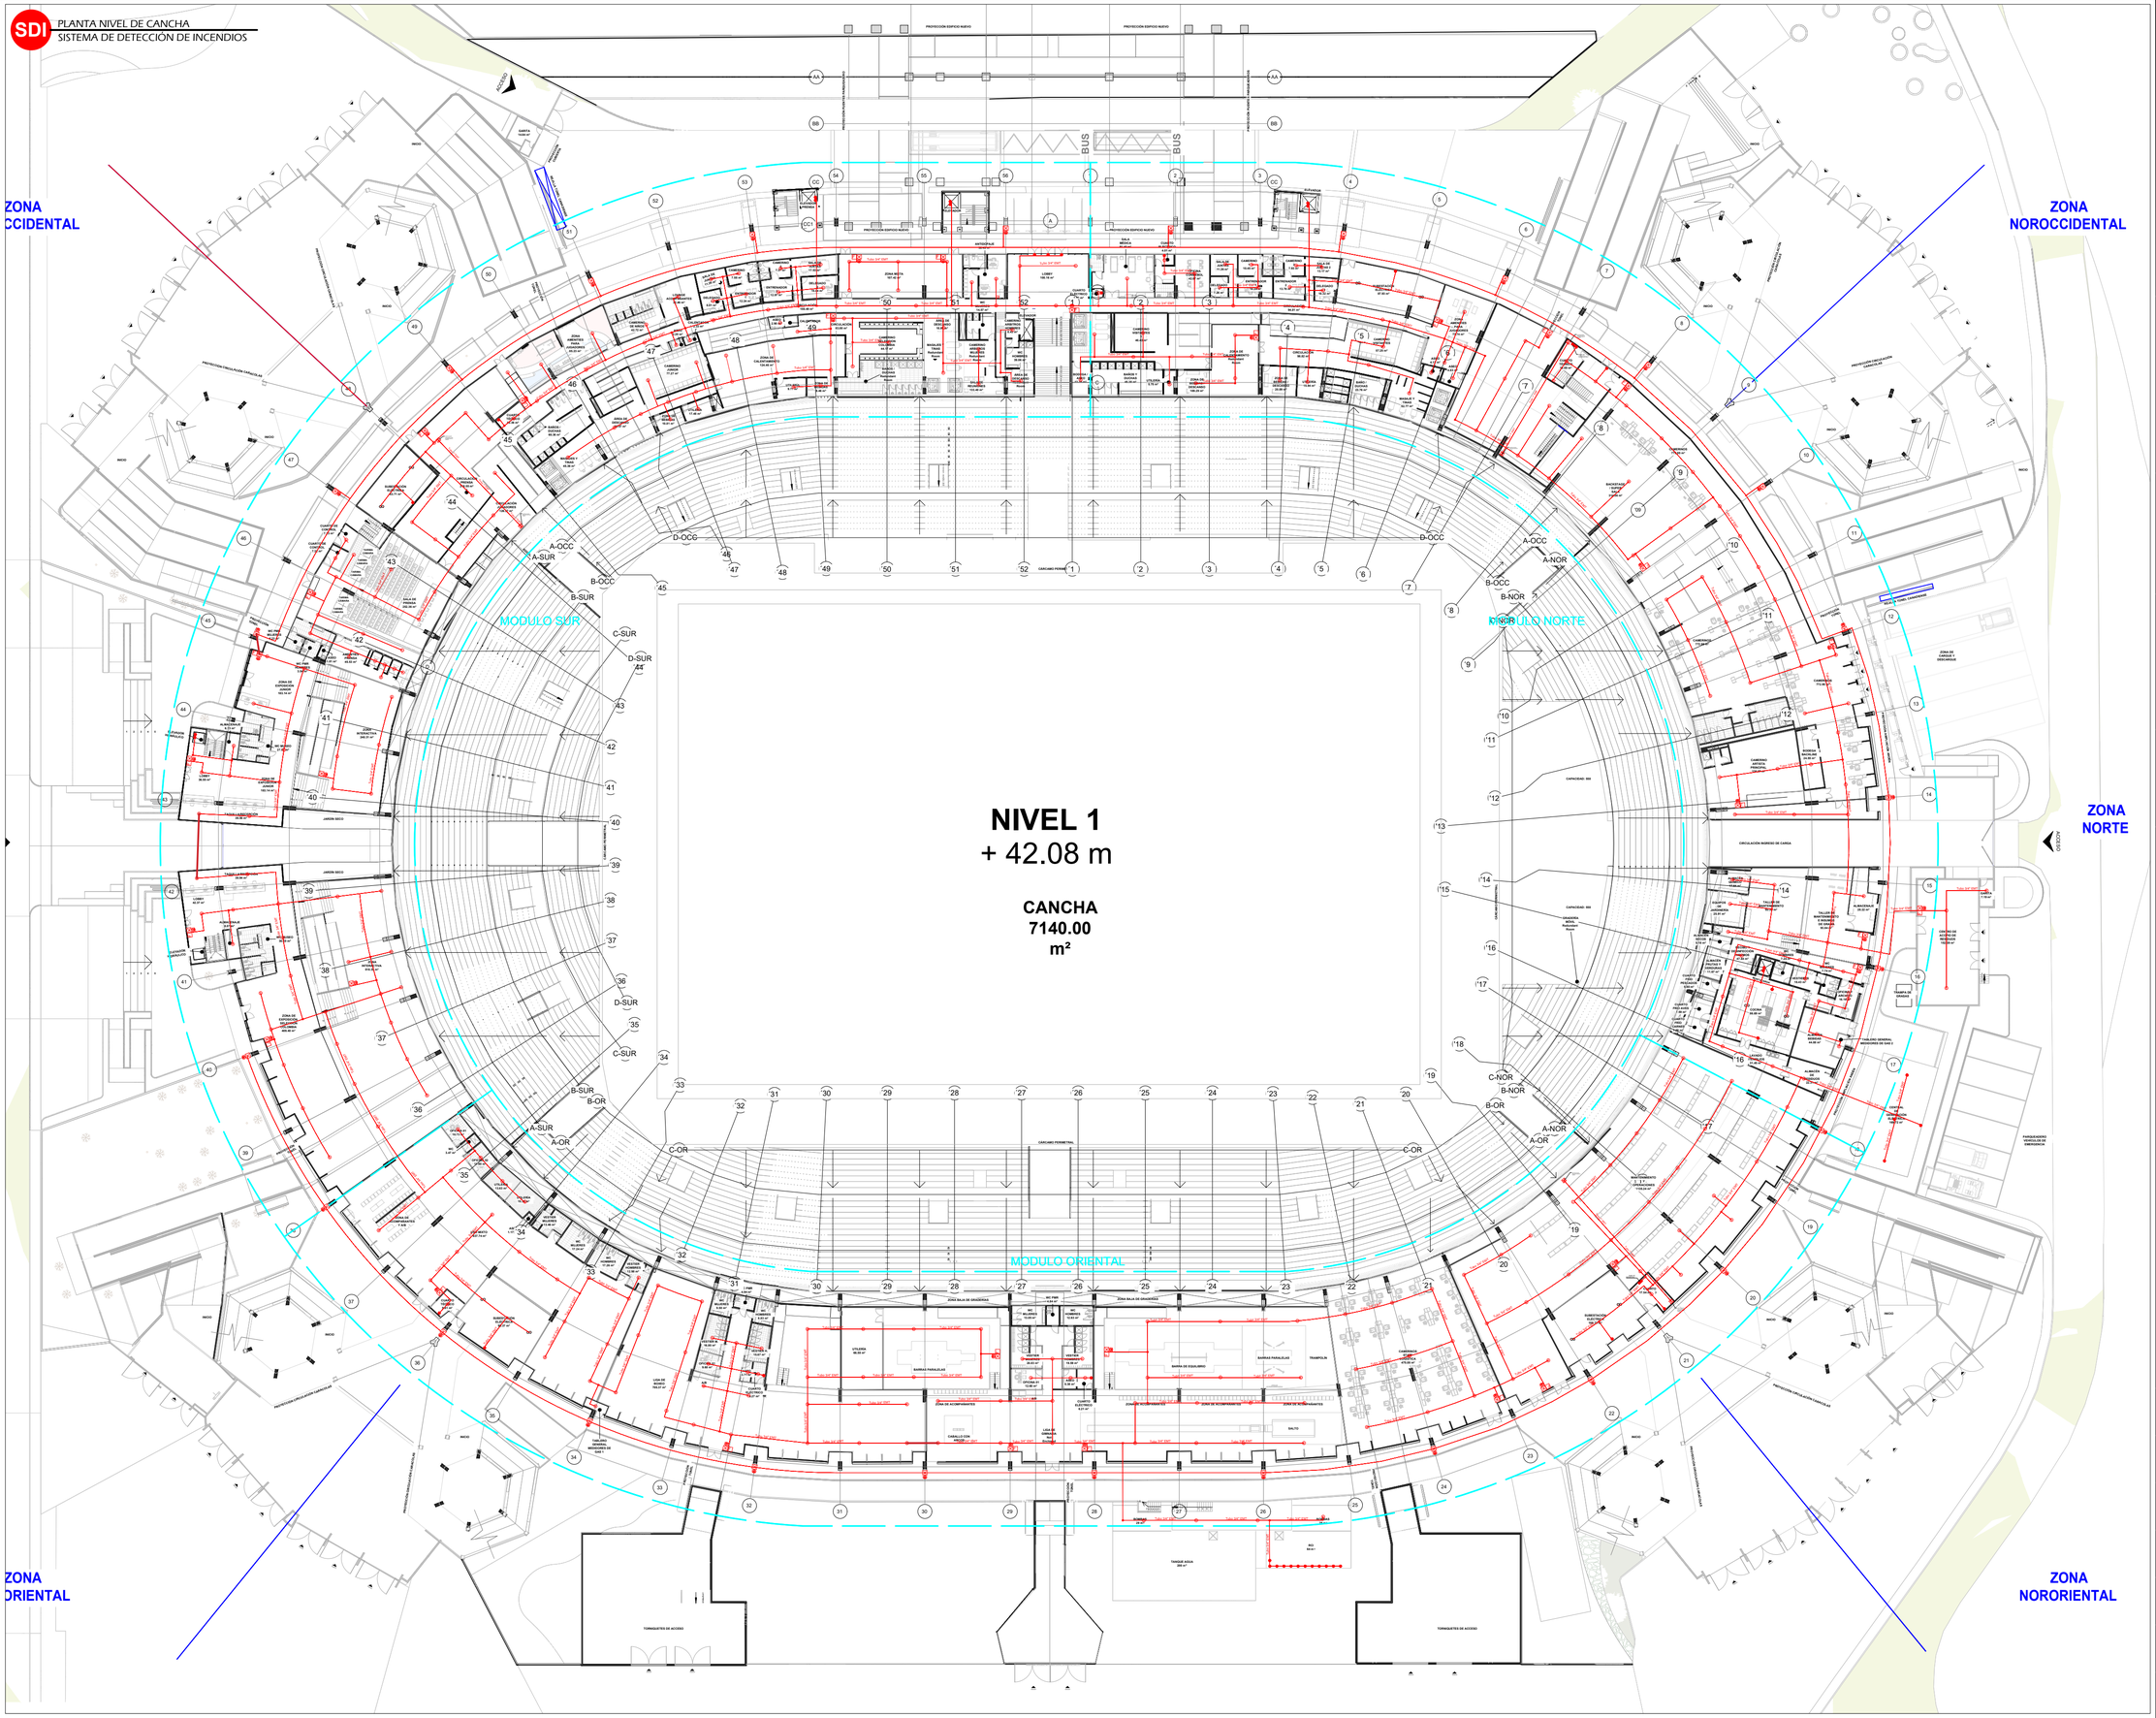

NIVEL 1
+ 42.08 m

CANCHA
7140.00
m²

PROYECTO:
SISTEMA DE DETECCIÓN DE INCENDIOS

UBICACIÓN:
Calle 46 #1 Sur - 45, Barranquilla, Atlántico

CONTIENE:
NIVEL 1 - NIVEL DE CANCHA

SISTEMA:
SISTEMA DE DETECCIÓN DE INCENDIOS

CONVENCIONES:

——	Tuberia EMT ¾"
H CO	Detector Térmico y CO
S H	Detector Humo y Térmico
S	Detector Humo
H	Detector Térmico
F	Estación Manual
G	Detector de GAS
MM	Modulo Monitor
MM	Modulo de control o Relé
	Parlante-Estrobo
	Parlante de techo
	Caja de 4"x4"
	Registro 50cm x 50cm
FACP	Panel de Incendio
AR	Anunciador remoto

DISEÑO:
Ing. Carlos Correa

DIBUJÓ:
Arq. Yahir Ortega Alvarez

REVISIÓN:
Ing. Nicolás Mussa

FECHA:
ABRIL - 2026

ESCALA:
1:350

PLANCHA No.:
1 - 6

ARCHIVO:
SDI_ROBERTO MELENDEZ 2026