**SDI** PLANTA NIVEL DE MEZANINE
SISTEMA DE DETECCIÓN DE INCENDIOS

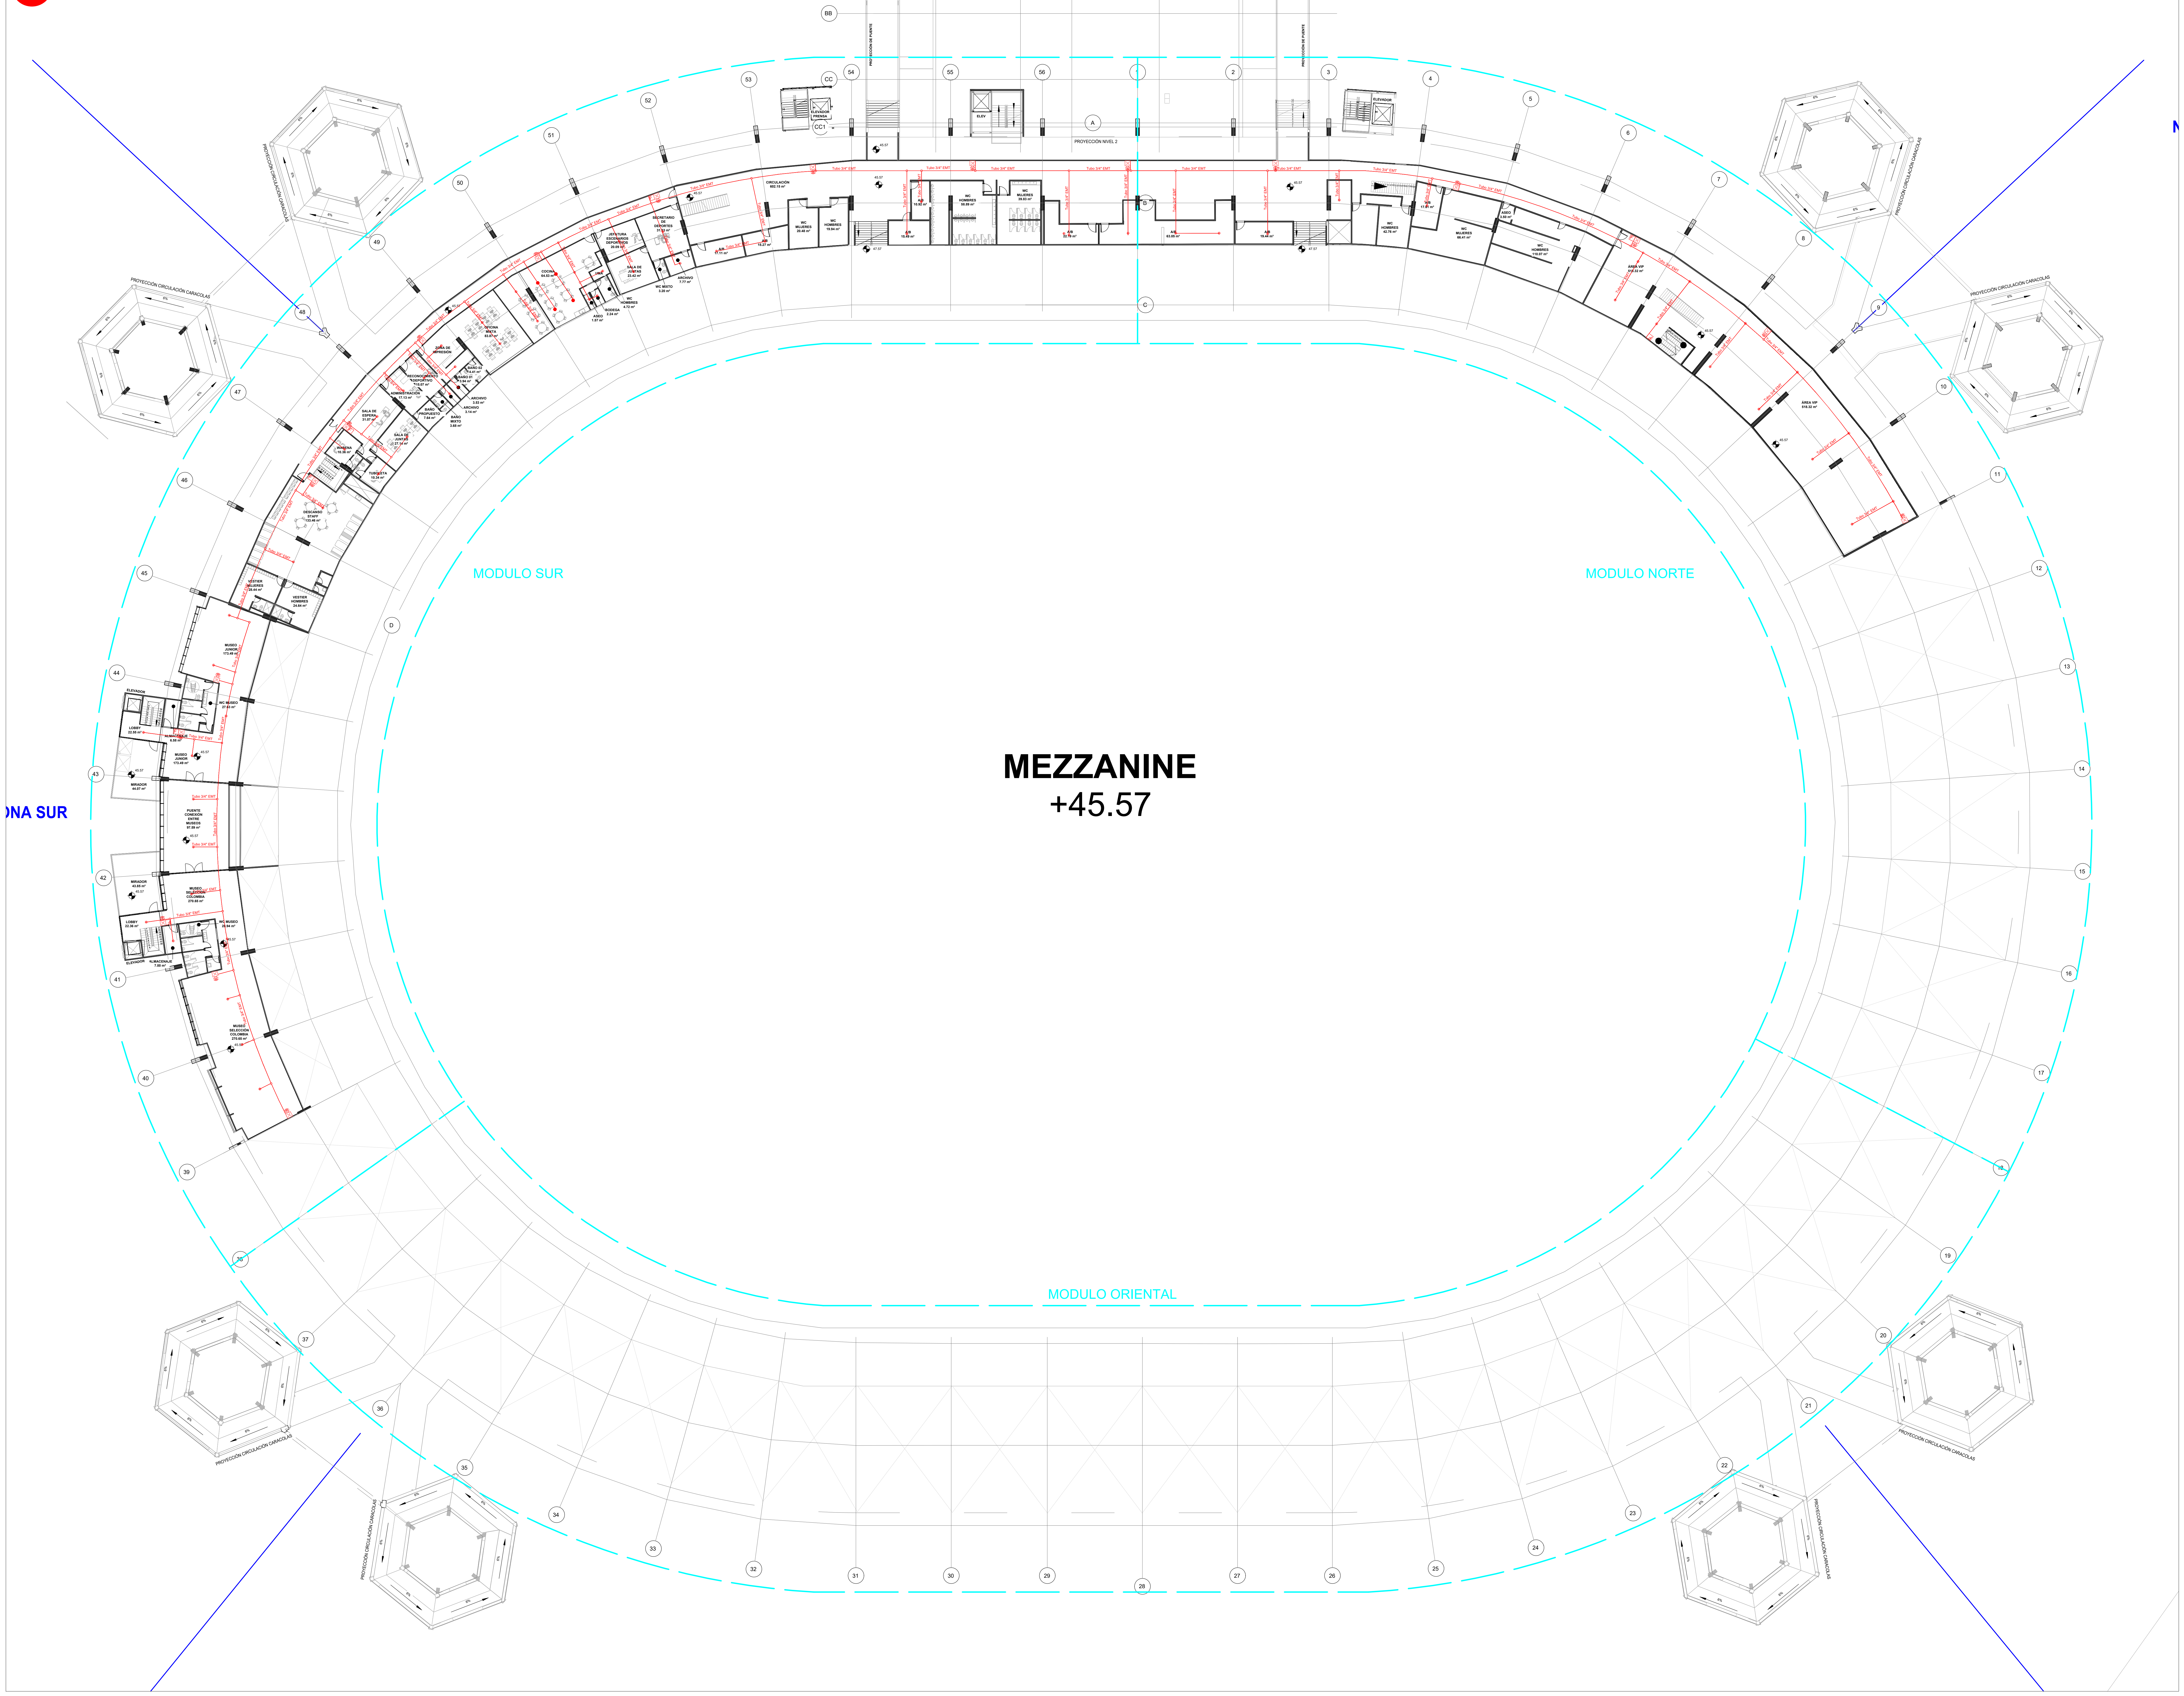

**GRUPO INTEGRA**
Confianza que conecta.
Ingeniería que protege.

PROYECTO:
SISTEMA DE DETECCIÓN DE INCENDIOS

UBICACIÓN:
Calle 46 #1 Sur-45,
Barranquilla, Atlántico

CONTIENE:
PLANTA NIVEL DE MEZANINE

SISTEMA:
SISTEMA DE DETECCIÓN DE INCENDIOS

CONVENCIONES:

| | |
|---|---|
| FACP | Panel de Incendio |
| ▭ | Fuente para sirena |
| — | Tubería 3/4" EMT/SCH40 |
| ● | Subidas / Bajadas de Tubería |
| ② | Sensor de Humo |
| ○ | Sensor de monóxido |
| ① | Sensor térmico |
| ○ | Sensor autónomo |
| ○ | Sensor de doble tecnología |
| EM | Estación Manual |
| ☒ | Sirena Estrobo |
| ☐ | Caja de paso |
| ▭ | Modulo de relevo |

DISEÑO:
Ing. Carlos Correa

DIBUJÓ:
Arq. Yahir Ortega Alvarez

REVISIÓN:
Ing. Nicolás Mussa

FECHA:
ABRIL - 2026

ESCALA:
1:500

PLANCHA No.:
3 - 6

ARCHIVO:
SDI_ROBERTO MELENDEZ 2026